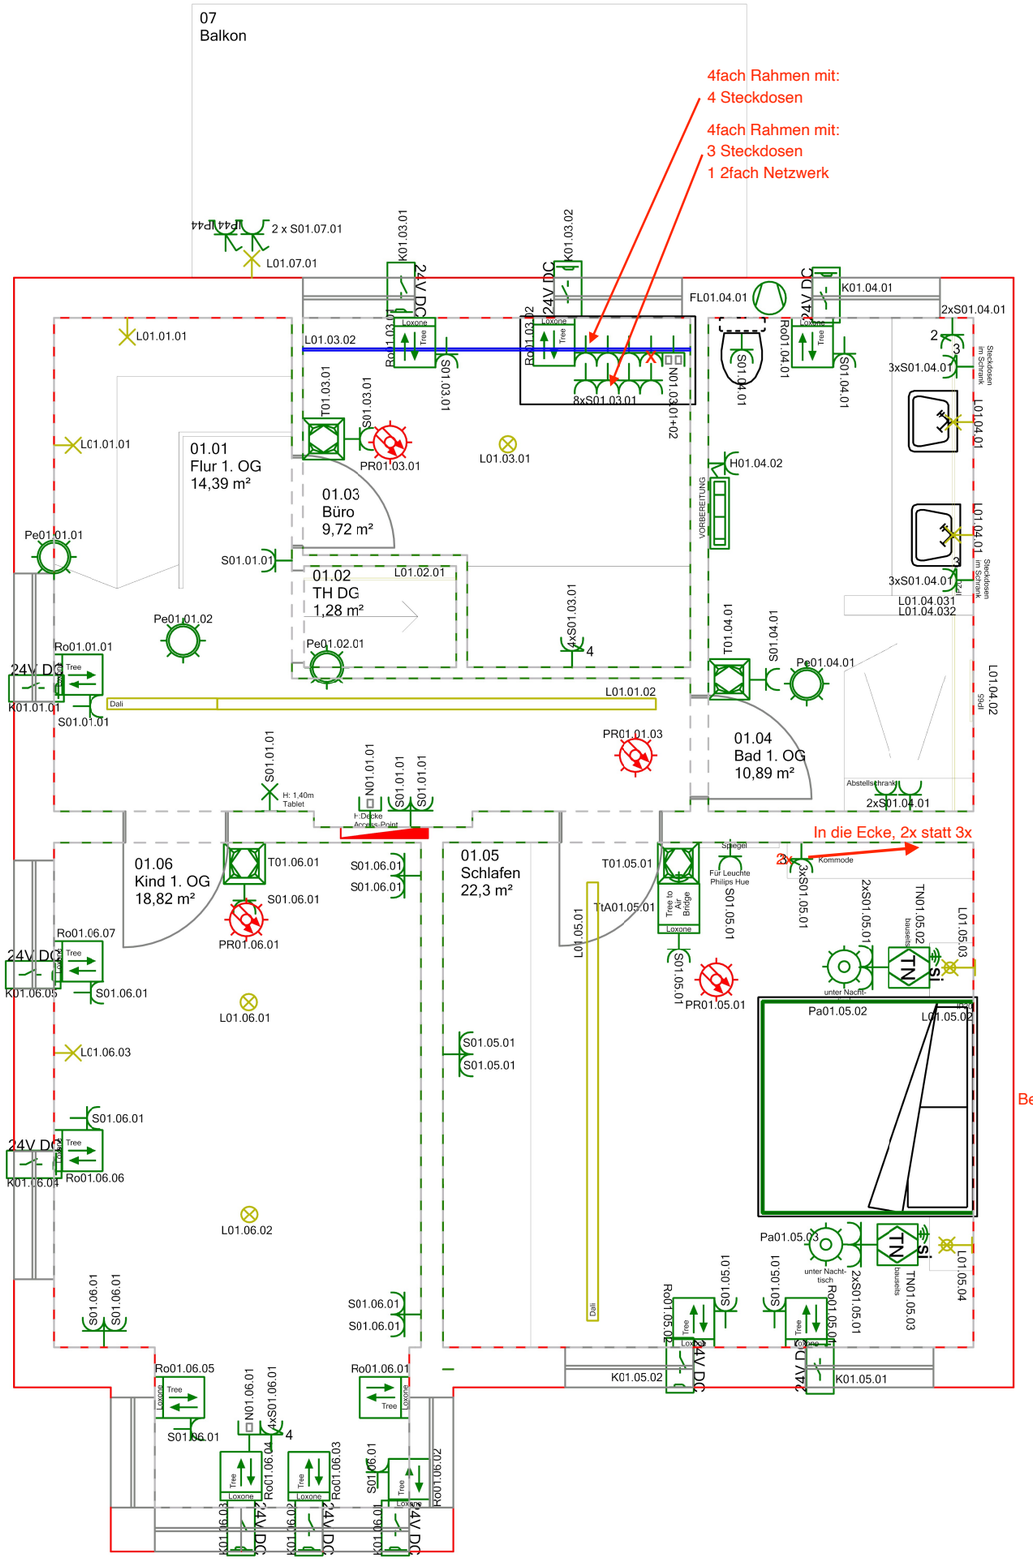

Leuchte

- Hängeleuchte, 24V DC, dimmbar
- LED Streifen (gelb=ww;blau=dw;grün=rgbw)
- Wandauslass für Leuchtenanschluss
- Stromschiene, isoLED Track 48, Weiß, Dali
- Deckenauslass für Leuchte, 230V AC, nicht dimmbar

Steckdose

- UP Schukosteckdose 1-fach mit Klappdeckel, schaltbar, IP44
- UP Schukosteckdose 2-fach waagerecht
- UP Schukosteckdose 1-fach
- Daten-Anschlussdose Cat.5 2x RJ45 AP
- Daten-Anschlussdose Cat.5 1x RJ45 AP
- für Tablet
- UP Schukosteckdose 4-fach
- UP Schukosteckdose 3-fach
- UP Schukosteckdose 2-fach
- UP Schukosteckdose schaltbar

Sensoren

- Touch Tree Weiß
- Tür- und Fensterkontakt, 24V DC
- Nano 2 Relay Tree
- Präsenzmelder Tree Weiß
- Präsenzmelder Deckeneinbau Tree Weiß
- Touch Nightlight Classic Air, Signalweiß
- Rauch- und Präsenzmelder Tree Weiß
- Tree to Air Bridge

Elektrogerät

- Feuchtraumlüfter, 230V AC

Raumheizkörper

- Handtuchheizkörper

Version zur Erstellung von Kabelliste
und Verteilerplanugn freigegeben

Datum Unterschrift

Version 1.1		21.04.2026	DSHP	Bearb.	21.04.2026 DSHP				DSHP Gebäudeautomation und Energie GmbH	1. Obergeschoss	Projekt: Weihs	=
Version 1.2		27.04.2026	DSHP	Gepr.	21.04.2026					Installationsplan	Nürnberg	+
Version 1.3		04.05.2026	DSHP	Stand							Anlage:	Zeichnungsnr.: Weih6011 / Blatt: / Anz.Bl:
Rev.	Änderung	Datum	Name	Norm		Urspr.	Ers.f.	Ers.d.				