


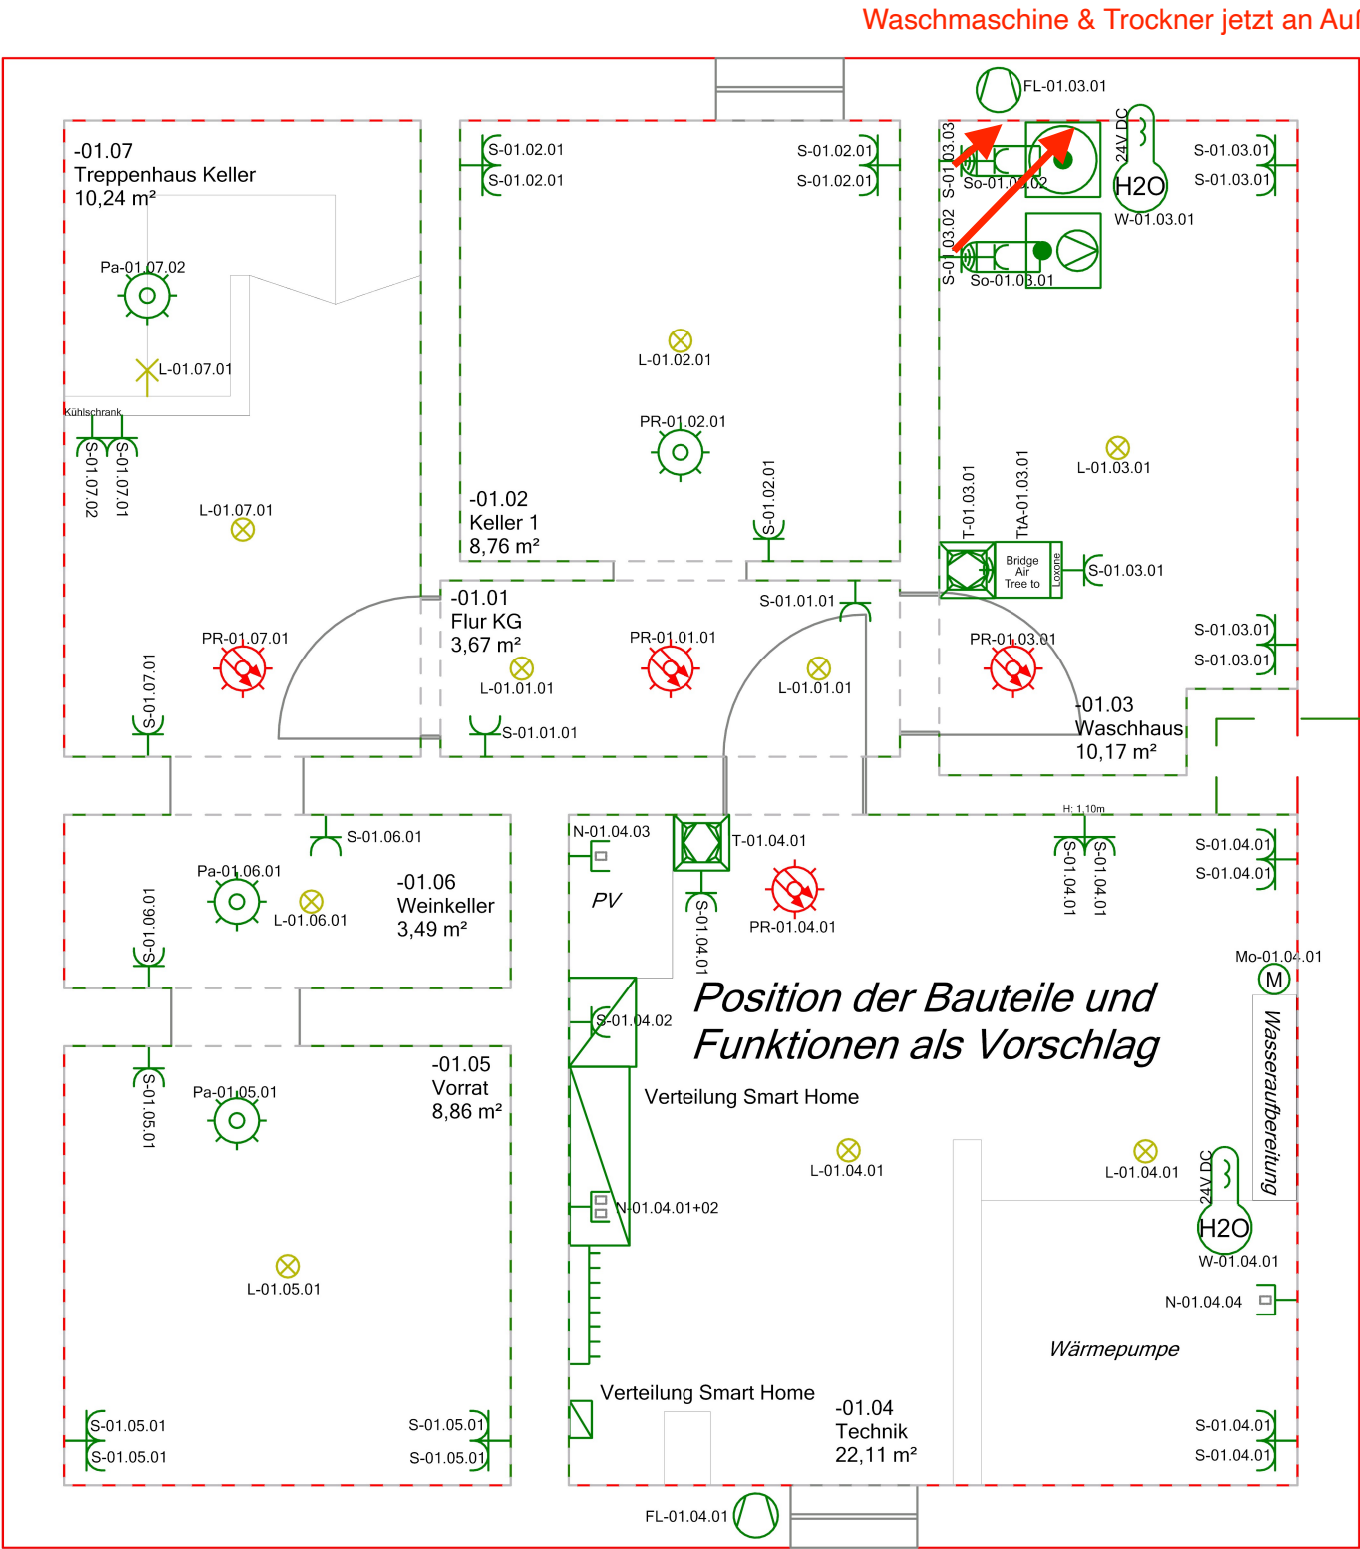

Leuchte	
	Deckenauslass für Leuchte, 230V AC, nicht dimmbar
	Wandauslass für Leuchtenanschluss
Sensoren	
	Präsenzmelder Tree Weiß
	Wassersensor 24V DC
	Smart Socket Air Typ F
	Touch Tree Weiß
	Rauch- und Präsenzmelder Tree Weiß
	Tree to Air Bridge
Elektrogerät	
	Waschmaschine
	Wäschetrockner
	Feuchtraumlüfter, 230V AC
Verteiler	
	Hausanschlusskasten
	3t-Zählerschrank 950x 800x205
	Standschaltschr. 2000x1200x400 +100 So
	Netzwerkschrank 12HE (T:450 x B:600 x H:635)
Steckdose	
	UP Schukosteckdose 2-fach waagerecht
	UP Schukosteckdose 1-fach
	Daten-Anschlussdose Cat.5 2x RJ45 AP
	Daten-Anschlussdose Cat.5 1x RJ45 AP
Elektromotor	
	Ansteuerung Magnetventil

Version 1.2		27.04.2026	DSHP	Bearb.	21.04.2026	DSHP	DSHP Gebäudeautomation und Energie GmbH	Kellergeschoss -01		Projekt: Weihs		=
Version 1.3		04.05.2026	DSHP	Gepr.	21.04.2026			Nürnberg				+
Version 1.4		15.05.2026	DSHP	Stand				Anlage:		Zeichnungsnr.:		Blatt:
Rev.	Änderung	Datum	Name	Norm			Urspr.	Ers.f.	Ers.d.		Weih6009	Anz.Bl: