


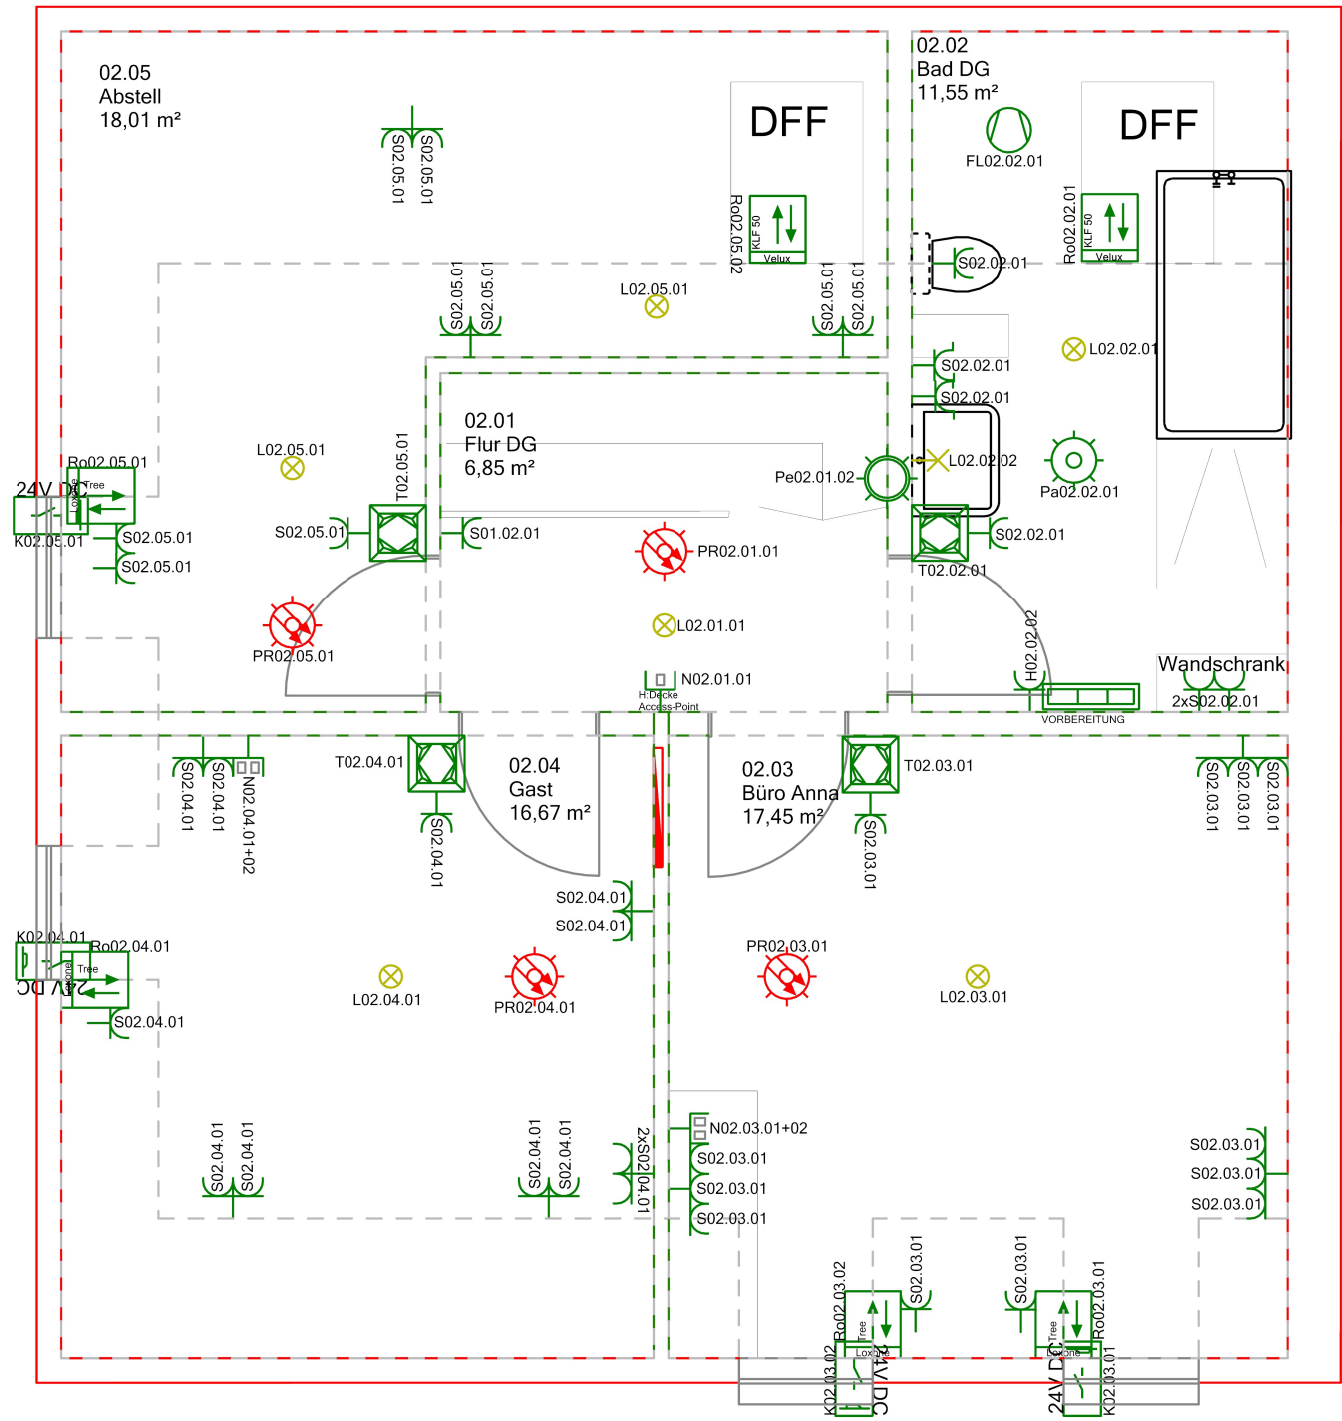

Leuchte	
	Wandauslass für Leuchtenanschluss
	Deckenauslass für Leuchte, 230V AC, nicht dimmbar
Steckdose	
	UP Schukosteckdose 2-fach waagrecht
	UP Schukosteckdose 1-fach
	Daten-Anschlussdose Cat.5 2x RJ45 AP
	Daten-Anschlussdose Cat.5 1x RJ45 AP
	UP Schukosteckdose mit Klappdeckel
	UP Schukosteckdose 3-fach waagrecht
Sensoren	
	Touch Tree Weiß
	Tür- und Fensterkontakt, 24V DC
	Nano 2 Relay Tree
	Präsenzmelder Deckeneinbau Tree Weiß
	Velux KLF50
	Präsenzmelder Tree Weiß
	Rauch- und Präsenzmelder Tree Weiß
Elektrogerät	
	Feuchtraumlüfter, 230V AC
Raumheizkörper	
	Handtuchheizkörper

Version 1.2		29.04.2026	DSHP	Bearb.	21.04.2026	DSHP	DSHP Gebäudeautomation und Energie GmbH	2. Obergeschoss			Projekt: Weihs		=	
Version 1.3		04.05.2026	DSHP	Gepr.	21.04.2026						Nürnberg		+	
Version 1.4		15.05.2026	DSHP	Stand							Anlage:	Zeichnungsnr.:		Blatt:
Rev.	Änderung	Datum	Name	Norm			Urspr.	Ers.f.	Ers.d.			Weih6012		Anz.Bl: