


- Allgemein:
- Elektroinstallation durch: Firma STONE & art S.Goller GmbH
 - Mit Loxone Alarmanlage
- 03.01 - Eingang/ Einfahrt
- 3 x Wandleuchte, 230V AC, AN/AUS , 1 Kreis, Leuchte bauseits
 - Positionen: Hausecke Einfahrt, Haustüre => L03.01.01
 - Vorbereitung Tor Einfahrt mit Motor => Mo03.01.02
 - Gartentür mit Türsummer => Mo03.01.01
- 03.02 - Garten West
- 3 x Gartenleuchte, 230V AC, AN/AUS, 1 Kreis, Leuchten bauseits
 - Position: Garten West => L03.02.01-03
 - Automatische Bewässerung, Vorbereitung 3 Kreise
 - 1 x schaltbare Steckdosen, 1 Kreis
- 03.03 - Garage/ Carport
- 1 x Deckenleuchte, 230V AC, AN/AUS, 1 Kreis, Leuchten bauseits
 - Position: Decke => L03.03.01
 - 1 x Wallbox Loxone, 11kW, ohne Abrechnungsfunktion
 - 2 x Steckdose für Ladung E-Bikes => S03.03.02+03
- 03.04 - Garten Ost
- 3 x Gartenleuchte, 230V AC, AN/AUS, 1 Kreis, Leuchten bauseits
 - Position: Garten => L03.04.01-03
 - Automatische Bewässerung, Vorbereitung 3 Kreise
 - Mähroboter, Integration bauseits
 - 1 x schaltbare Steckdosen, 1 Kreis => S03.04.01

Elektromotor	
	Motor Tor Einfahrt
Leuchte	
	Deckenauslass für Leuchte, 230V AC, nicht dimmbar
	Wandauslass für Leuchtenanschluss
Steckdose	
	UP Schukosteckdose 1-fach mit Klappdeckel, schaltbar, IP44
	UP Schukosteckdose 1-fach
	Daten-Anschlussdose Cat.5 1x RJ45 AP
Sensoren	
	Präsenzmelder Tree Anthrazit
	Motorschloss/ Türsummer
	Bewegungsmelder 24V
	Wallbox 11kW 16A Tree
	Wetterstation Tree
	Touch Tree Anthrazit
	Intercom Signalweiß
	Alarmsirene Tree
	NFC Code Touch Tree Signalweiß
Audio- und Videosystem	
	Videokamera, PoE

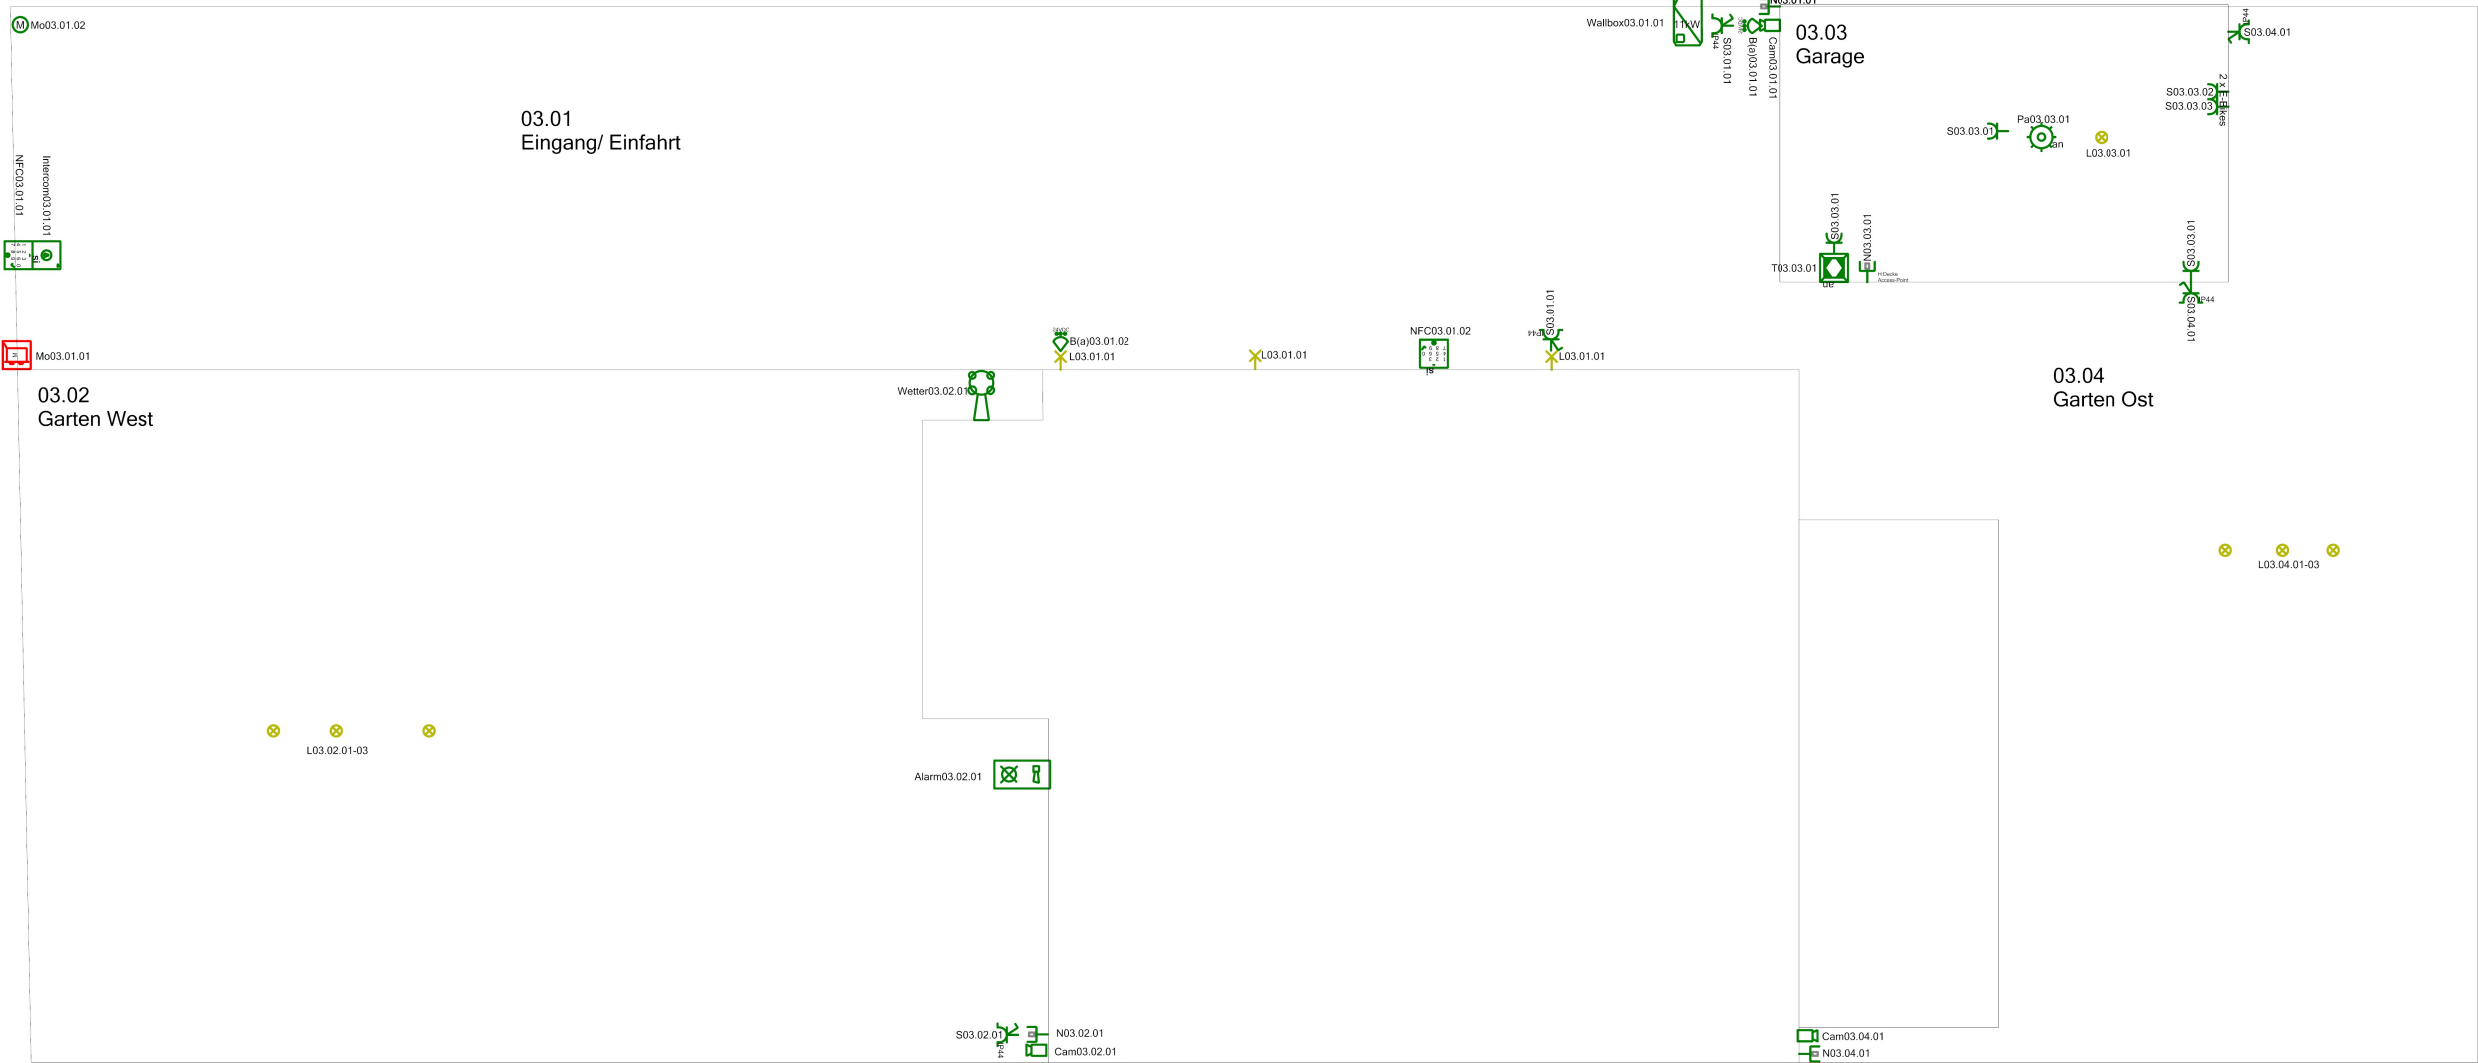

Version 1.2		29.04.2026	DSHP	Bearb.	21.04.2026	DSHP	DSHP Gebäudeautomation und Energie GmbH	Außenbereich Installationsplan		Projekt: Weihs		=	
Version 1.3		04.05.2026	DSHP	Gepr.	21.04.2026					Nürnberg		+	
Version 1.4		15.05.2026	DSHP	Stand						Anlage:	Zeichnungsnr.:		Blatt:
Rev.	Änderung	Datum	Name	Norm			Urspr.	Ers.f.	Ers.d.		Weih6013		Anz.Bl: